


CONCEPT, NOT FOR FABRICATION

REV	DESCRIPTION	DATE	BY
P3	Concept sheet	2026-09-25	AC

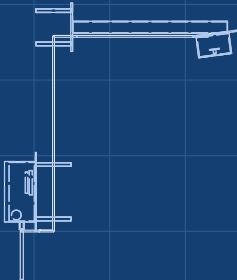


TOP VIEW
Scale 1:25



FRONT VIEW
Scale 1:25

RIGHT VIEW
Scale 1:25

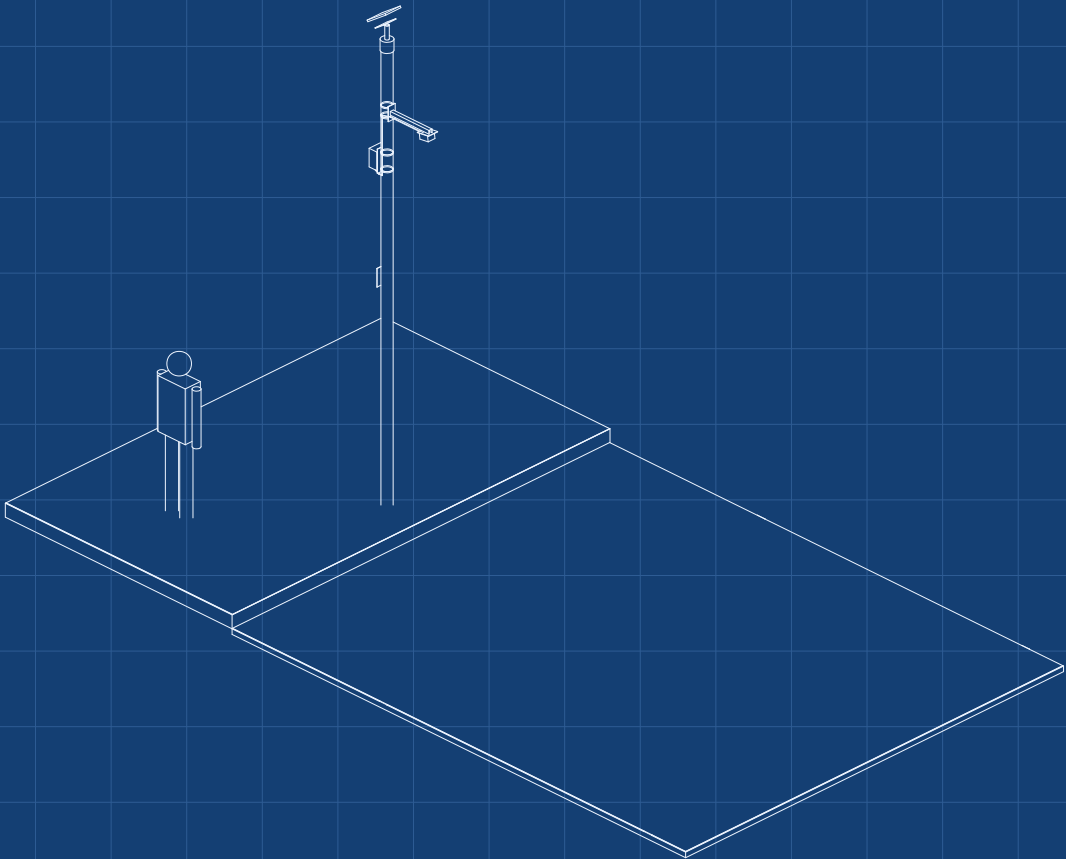

ISOMETRIC VIEW
Not to scale; grey is for scale

KEY FIGURES

Thermal array 32 x 24 px, 110 deg across the street
Footprint -4.4 to 8.3 m across, 6 to 7 m along
Counts people, bikes, vehicles; 15 min bins
No images leave the device; 7.6 px/m at head height
0.10 W from the cell; 6.2 days without sun
Parts \$253 vs \$275 budget (indicative)

CURBCOUNT

Privacy-safe street counter concept

DRAWING NO. CBC-DWG-010		REV P3	SHEET 1 of 1	SIZE ANSI B
SCALE 1:25	UNITS mm	PROJECTION 	DATE 2026-09-25	DRAWN Amish Chadha
MATERIAL / NOTES Massing model for concept communication				
Licensed CERN-OHL-S-2.0 · Design Molecule Lab · designmolecule.com			Generated from cad/src; do not edit by hand	