
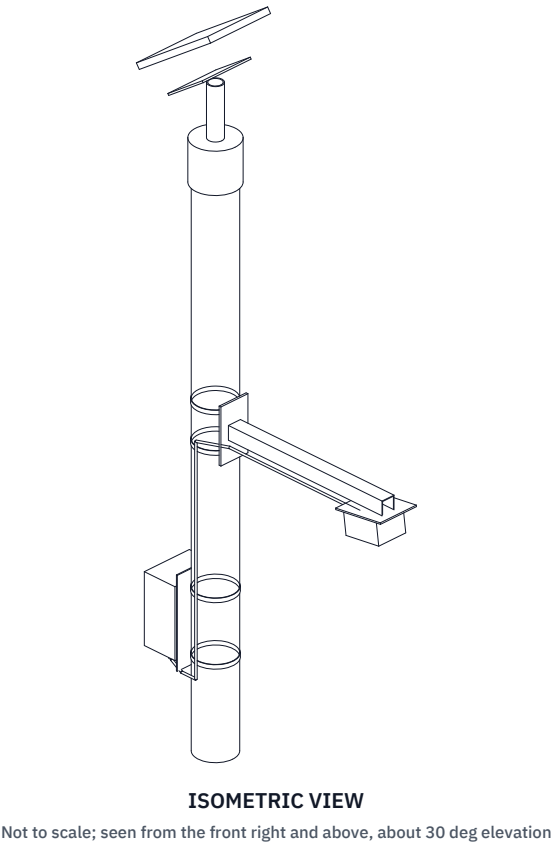


CONCEPT, NOT FOR FABRICATION
PRELIMINARY, NOT FOR FABRICATION

CurbCount · github.com/BoujeeEnjinia1701/curbcount

REV	DESCRIPTION	DATE	BY
P1	Preliminary GA for TRL 3 (from cad/src/model.py)	2026-09-25	AC
P2	DDR-002: 6 W panel, one cell, no head processor	2026-09-25	AC

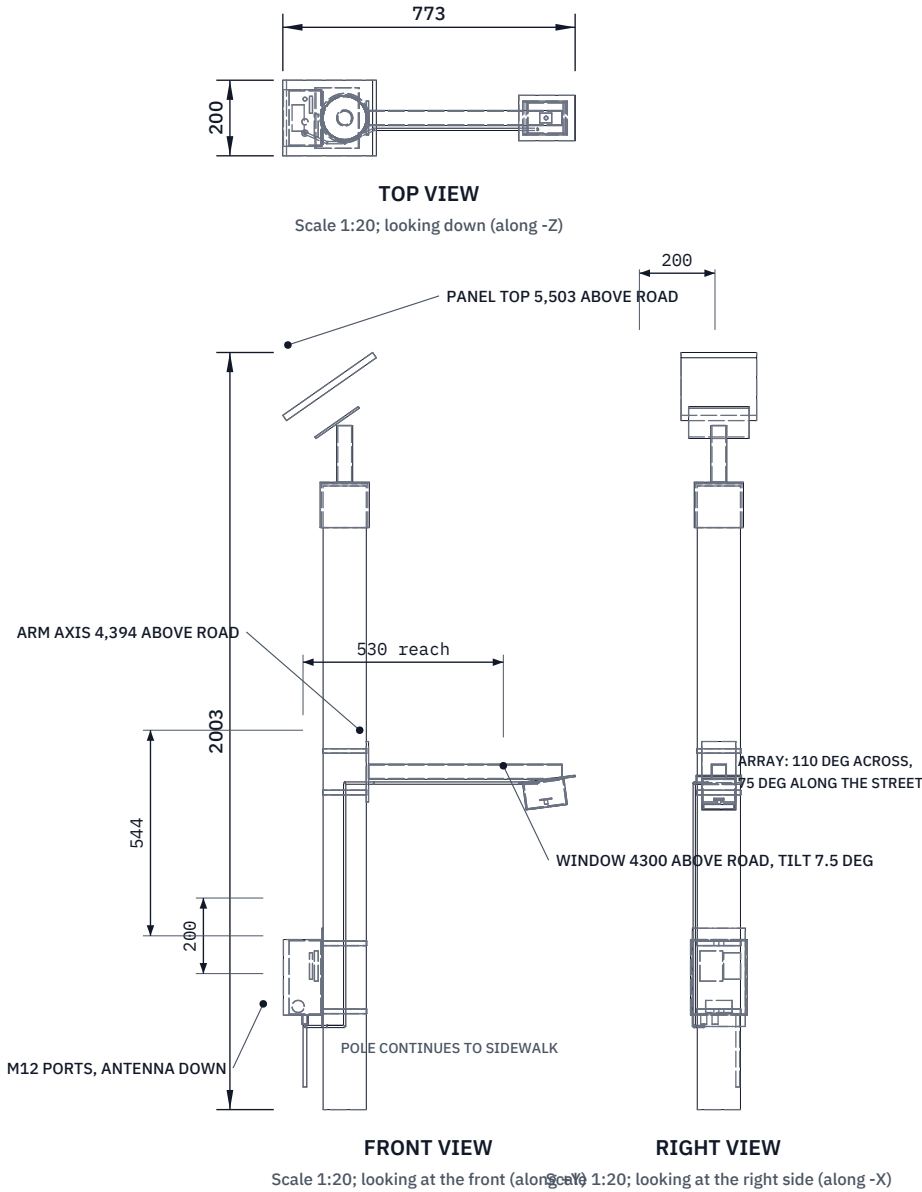

MAIN DIMENSIONS AND INTERFACES (MM)

Pole 114.3 OD, 450 behind the curb (site supplied, not in BOM)
Head 110 x 90 x 70, window 4300 above road, tilt 7.5 deg
Arm 40 x 40 x 2 Al, 512 long; reach 530 from pole axis
FieldNode enclosure 150 x 90 x 200, center 3850
Panel 6 W (FieldNode) 290 x 200, tilt 35 deg on a 120 sleeve
Four 12 mm stainless bands; no drilling of the pole
M12 5-pin cable, enclosure port to head (FieldNode pinout)
Footprint -4.4 to 8.3 m across the street (CBC-CAL-001)
Notice plate 150 x 200 at 2600 (not drawn); lanyards on panel and head

CURBCOUNT

github.com/BoujeeEnjinia1701/curbcount

General arrangement

DRAWING NO. CBC-DWG-001			REV P2	SHEET 1 of 1	SIZE ANSI B
SCALE 1:20	UNITS mm	PROJECTION 	DATE 2026-09-25		DRAWN Amish Chadha
MATERIAL / NOTES Aluminium mounts, ASA head; bought-in parts per bom/bom.csv. PRELIMINARY, NOT FOR FABRICATION					
Licensed CERN-OHL-S-2.0 · Design Molecule Lab · designmolecule.com				Generated from cad/src; do not edit by hand	